


[redacted]

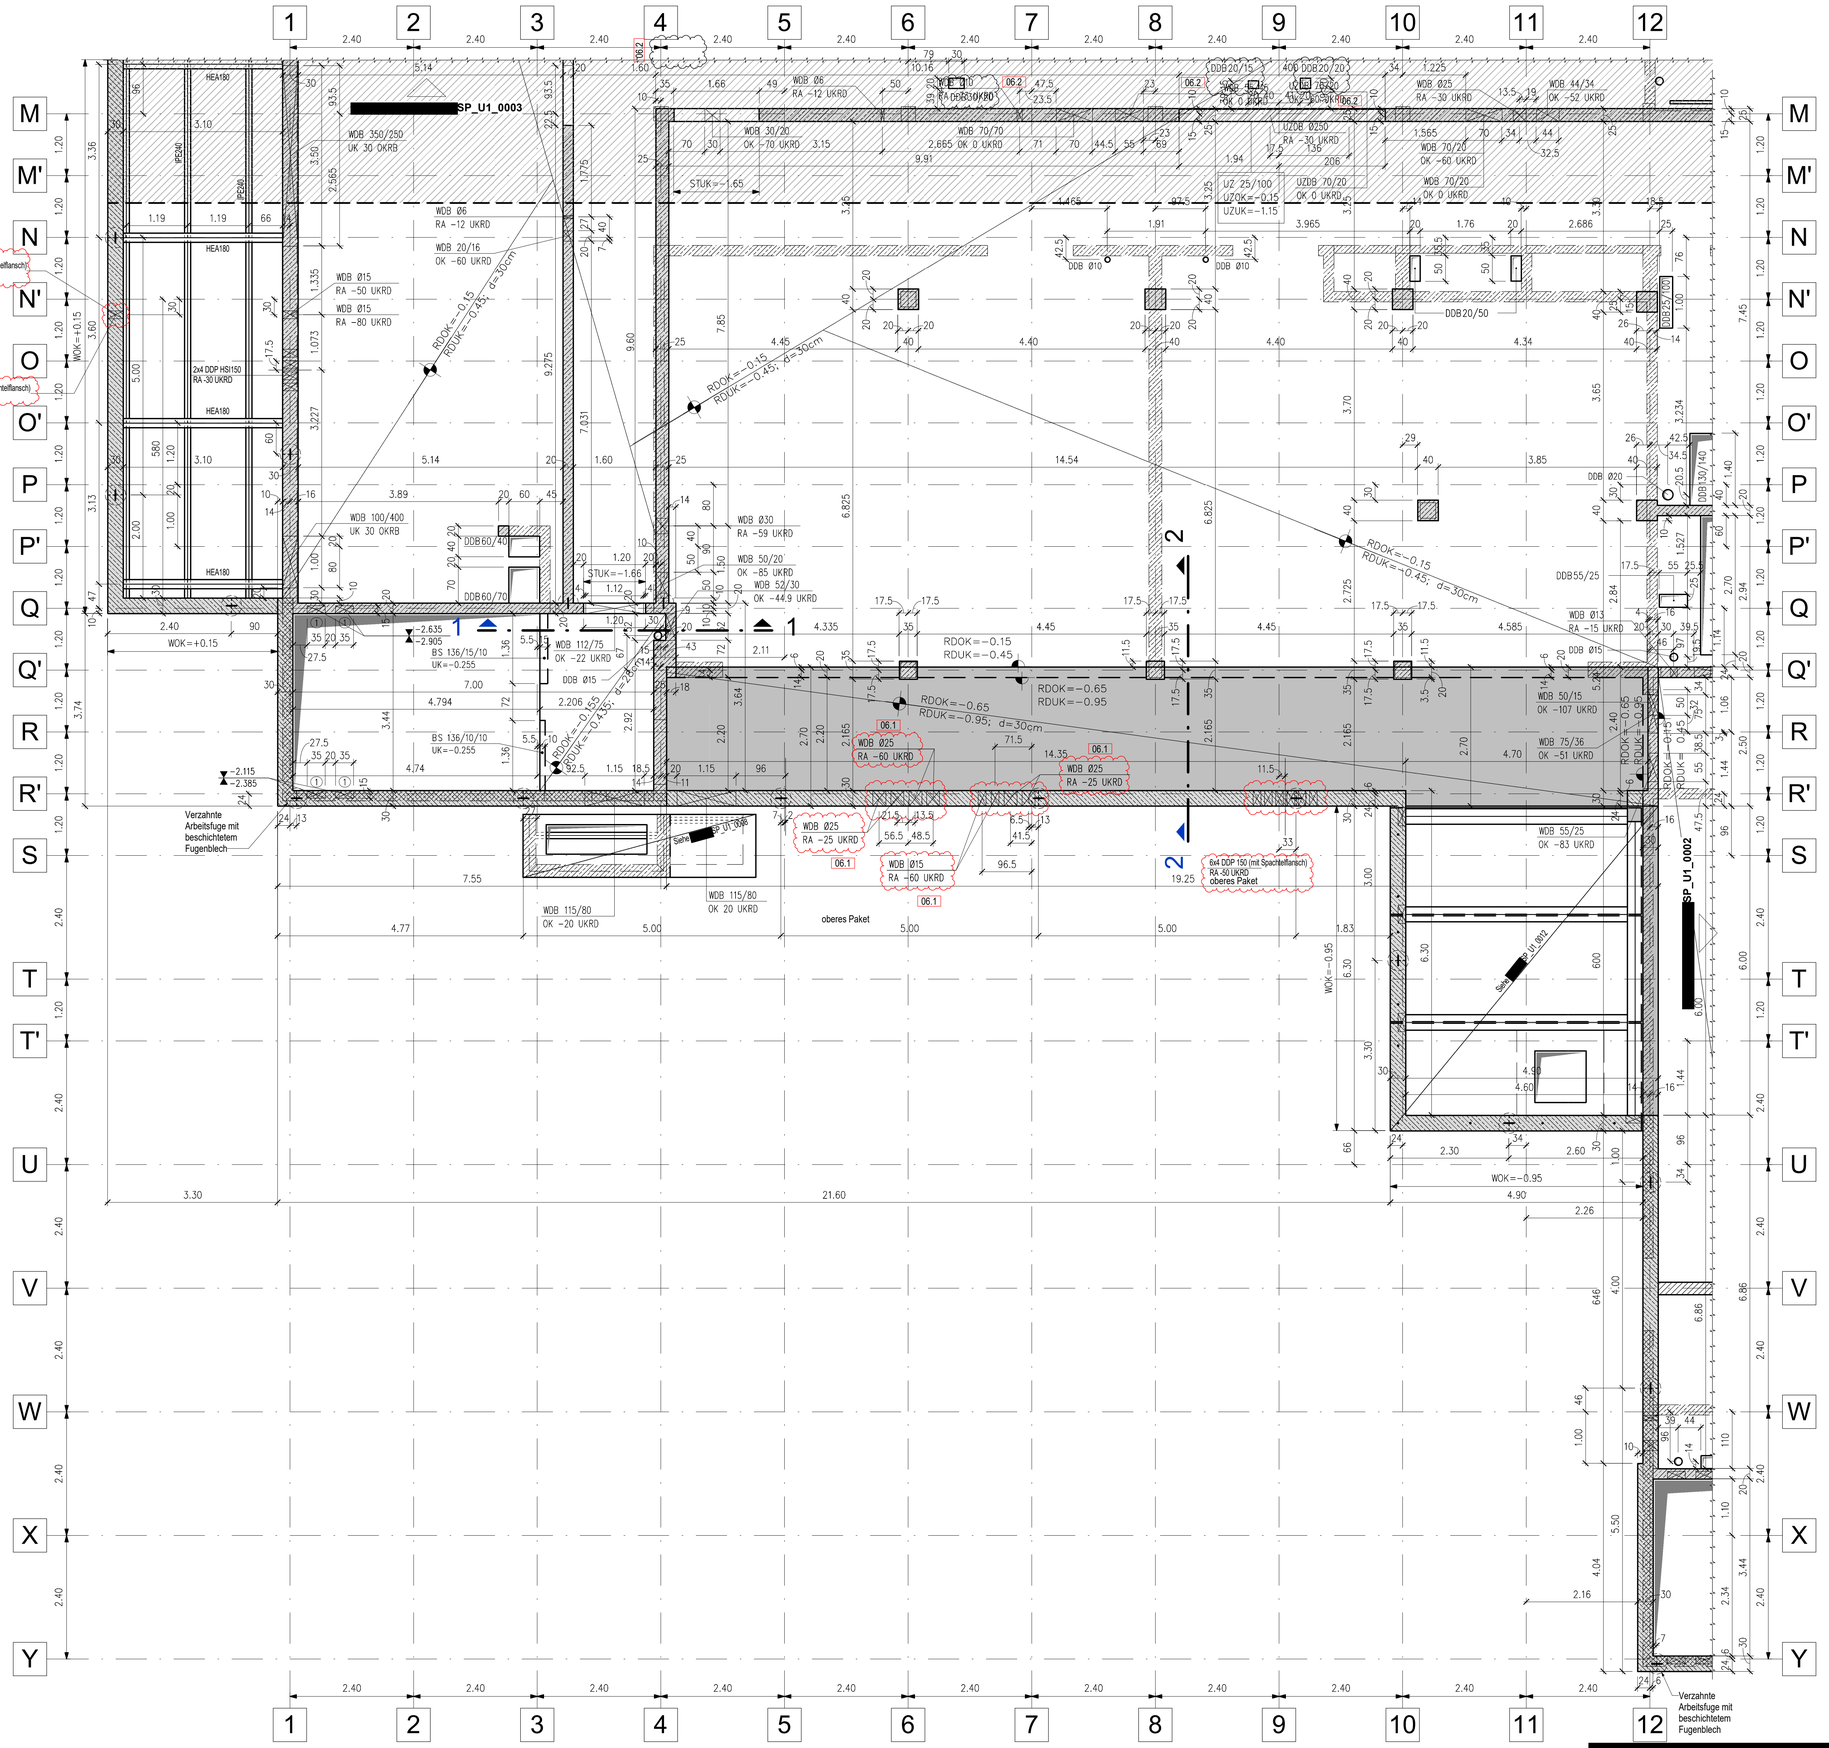

SCHNITT 1-1
M 1 : 50

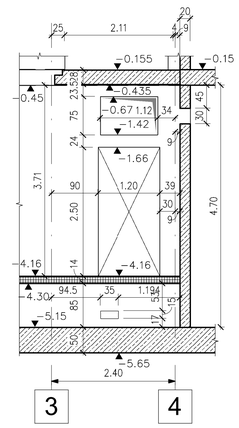

SCHNITT 2-2
M 1 : 50

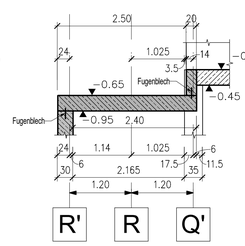

Beispiel:
Bei unterschiedlichen Deckenhöhen beidseitig eines Wanddurchbruchs ist für UKRD/OKRB die UK/OK der Decke auf der Seite der Markierung zu nehmen.



-NEU

-in Klärung

LEGENDE

- Stahlbeton
- Stahlbeton-Fertigteile
- Magerbeton
- Stahlbauteile im Detail
- Tragende Mauerwerk
- Brettsperrholz (BSP)
- tragende Wände **oberhalb** der betrachteten Decke
- WU-Beton

Darstellung Wände **unterhalb** der betrachteten Decke:
- Nichttragende Wände: werden nicht dargestellt.
- Tragende Wände: gemäß ihrer Ausführung

Darstellung Wände **oberhalb** der betrachteten Decke:
- Nichttragende Wände: werden nicht dargestellt.
- Tragende Wände: gestrichelt

- Pflaster
- Wärmedämmung
- Erde / Gelände
- EBT

Stb.	Stahlbeton	RDOK	Rohdeckenoberkante
FT	Fertigteil	RDUK	Rohdeckenunterkante
WD/DÄ	Wärmedämmung	RPOK	Rohparapetoberkante
EBT	Einbauteil	STUK	Sturzunterkante
UZ	Unterzug	UZUK	Unterzugunterkante
OZ	Oberzug	UZOK	Überzugoberkante
TRH	Treppenhaus	HFT	Halbfertigteil
UK	Unterkante	RD	Rohdecke
OK	Oberkante	AF	Arbeitsfuge
DDB/WDB	Decken-/Wanddurchbruch		
DS/WS	Decken-/Wandschlitz		
DA/WA	Decken-/Wandaussparung		

Tragende Mauerwerk
Tragende Mauerwerkswände in UG - HLZA 12, Ila, Rohdichteklasse 1,8kg/dm³, d= 24cm.
Öffnungen in tragenden Wänden sind aus dem Architektenplan ersichtlich

Revisionswolke
Revisionswolken in nicht freigegebenen Plänen weisen auf eine klärungsbedürftige Stelle hin.
Revisionswolken in freigegebenen Plänen weisen auf eine Änderung in der Zeichnung hin.

Schnittbezeichnung
Schnitte und Details, die in der Zeichnung angegeben sind, sich jedoch auf einem anderen Plan befinden, werden in einer Hinweisbox neben dem Plankopf zusammengefasst. Es wird dort auf den zugehörigen Plan verwiesen.

Detailbezeichnung
Schnitte und Details, die in der Zeichnung angegeben sind, sich jedoch auf einem anderen Plan befinden, werden in einer Hinweisbox neben dem Plankopf zusammengefasst. Es wird dort auf den zugehörigen Plan verwiesen.

Darstellung Deckendurchbrüche
Deckendurchbrüche (DD) und Deckenaussparungen (DA) werden im Grundriss wie folgt dargestellt. Angabe der Abmessungen in mm bei runden Durchbrüchen und in cm bei rechteckigen Druchbrüchen und Aussparungen.

Darstellung Wanddurchbrüche
Wanddurchbrücke (WD) und Wandaussparungen (WA) werden im Grundriss wie folgt dargestellt. Angabe der Abmessungen in cm mit dem Format bei WA: b/ht/l.
Bei allen Wanddurchbrüchen und -aussparungen ist die Höhenkote der Ober- bzw. Unterkante anzugeben.

DDB ⌀100

DDB 40/30

DA 40/30/10


WDB 100/50
OK -100 UKRD

WA 100/40/10
OK -100 URKD

Sollrissfugenelement

Sonstige Materialien sind in der Zeichnung angegeben. Für bezeichnete Produkte können gleichwertige, bauaufsichtlich zugelassene Produkte verwendet werden.

[redacted]

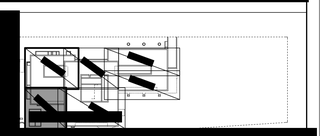

[redacted]

Maßstab	Planinhalt	Blattschnitt
1:50	Untergeschoss 1	2

[redacted]